CLIENT PROFILE

YUMEKO JABAMI

CLIENT NAME:-
YumekoJabami
FROM:- Kakegurui
AGE:- 18 years
Occuption:-
Student at Hyakkaou
Private Academy
ERSONALITY:-
Thrill seeker charis-
matic unpredictable



HOBBIES & INTERESTS

- GAME GAMBLING (cards, poker, roulette theme)
- MIND GAME & STRATEGY
- COLLECTING ITEMS (LUXURY)
- ENJOYS THE INTENSE, THEATRICAL ENVIRONMENT

LIFESTYLE

- ELITE PRIVATE SCHOOL ENVIRONMENT
- SPENDS TIME GAMBLING AND ANALYZING OPPONEN
-TS
- LATE NIGHT STRATEGIC THINKING
- VALUE EXCITEMENT OVER COMFORT
- MAINTAINS A POLISHED REFINED APPEARANCE

ERSONALITY TRAITS

Highly intelligent and observent
Love risk and high-stakes situation
Confident and bold
Mysterious and emotionally intense
Elegant but dangerously playfull
Drawn to drawn and psychological tension

Design implication:
Luxurious,+ Dramatic+ Slightly dark


NAME:- URVI G ERAGOLA	SIGNATURE AND REMARKS	MARKS:-
ROLLNO:- 14		
YEAR&CLASS:- FYBVOC		

NAME: URVI G ERAGOLA

YEAR: FYBVOC.

ROLL NO: 14

MASTER BEDROOM

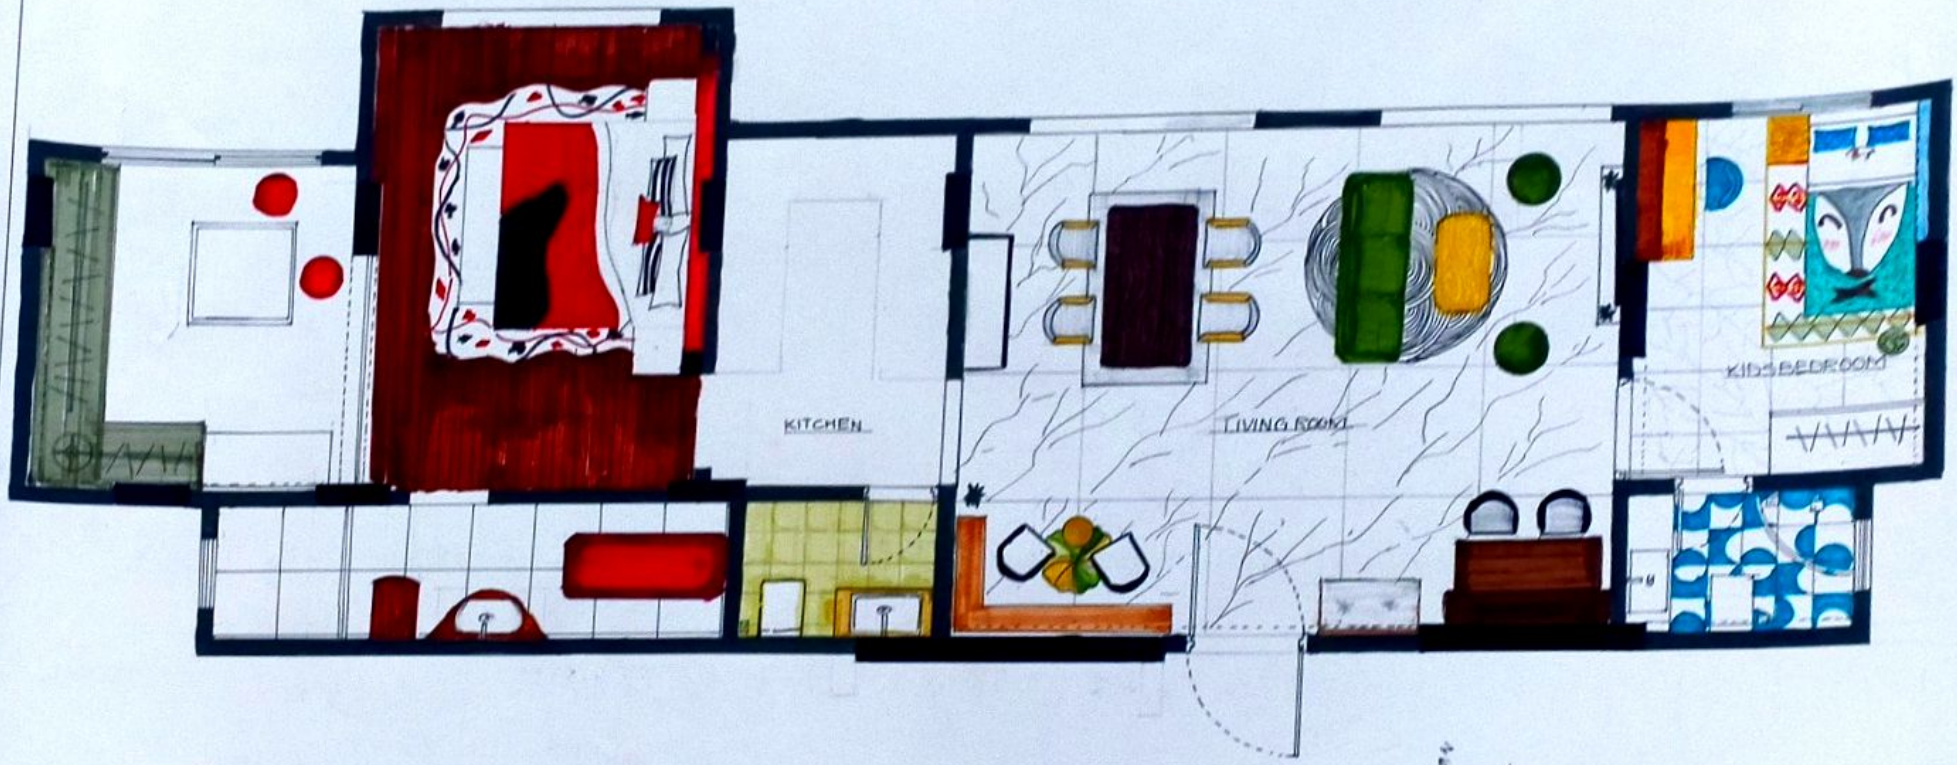

RACHANA SANSADS
ACADEMY OF ARCHITECTURE
B. VOC. (Interior Design)
MUMBAI


TOPIC: 2BHK MASTER BEDROOM PLAN

NOTE: ALL DIMENSIONS AND LEVELS ARE IN MILLIMETERS

SHEET NO.:	NAME : URVI G ERAGOLA		SIGNATURE AND REMARKS:
SCALE : 1:25	YEAR AND CLASS : FYBVOC	MARKS :	
DATE :	ROLL NO. : 14		

SCHEDULE

SB	HEIGHT	PARTICULARS	MODULE	LOCATION
SB1	600	1 SWICHT FOR L1, L3 1 SWICHT FOR L2, L4 1 SWICHT FOR FAN F1 1 SWICHT FOR REGULATOR 1 SWICHT FOR SOCKET (A.C) 1 SWICHT FOR SOCKET	6	NEAR THE ENTRANCE OF BED ROOM BESIDE THE BED
SB2	1350	1 SWICHT FOR L5, L6 1 SWICHT FOR L11, L12, L13 1 SWICHT FOR SOCKET 1 1 SWICHT FOR GEYSER 1 SWICHT FOR EXHAUST FAN	6	OUT SIDE BATHROOM WALL
SB3	1350	1 SWICHT FOR L7, L10 1 SWICHT FOR L8, L9 1 SWICHT FOR SOCKET (A.C) 1 SWICHT FOR SOCKET	4	IN SIDE WARDROBE ROOM ON WALL

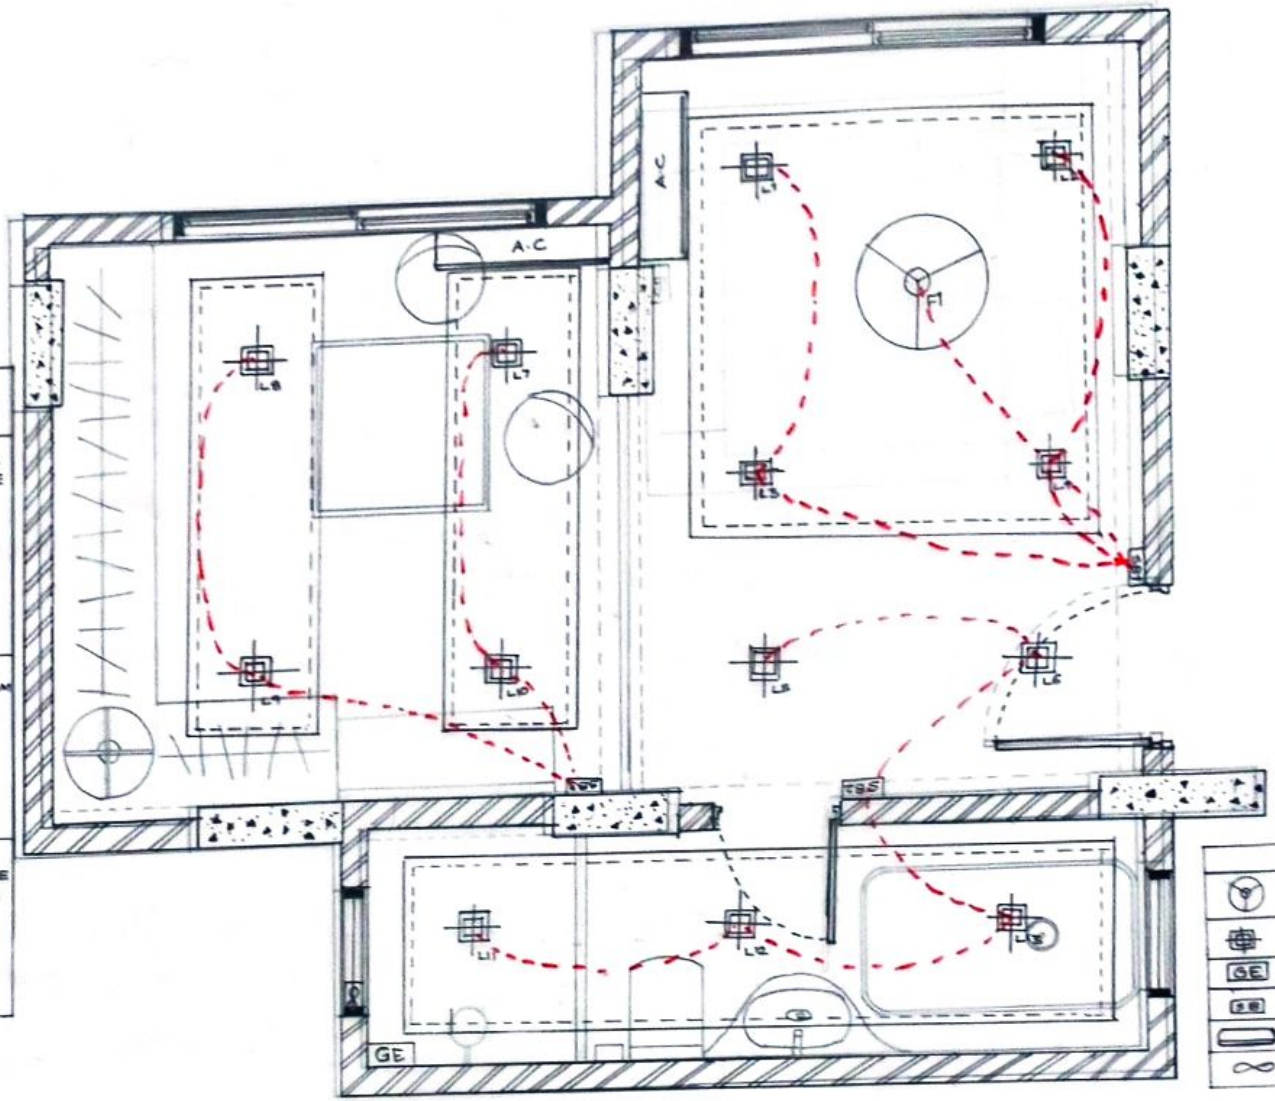


INDICATION		
	F	FAN
	L	PANEL LIGHT
GE	GE	GEYSER
SB	SB	SWITCH BOARD
	A C	AIR CONDITIONER
	-	EXHAUST FAN

RACHANA SANSAD ACADEMY OF ARCHITECTURE BVOC (INTERIOR DESIGN) MUMBAI

TOPIC: ELECTRICAL LOOPING WITH SCHEDULE

BEDROOM PLAN

SHEET NO	NAME URVI G BRAGOLA	SIGNATURE AND REMARKS:
SCALE 1:15	YEAR AND CLASS FY BVOC	MARKS:
DATE	ROLL NO 74	

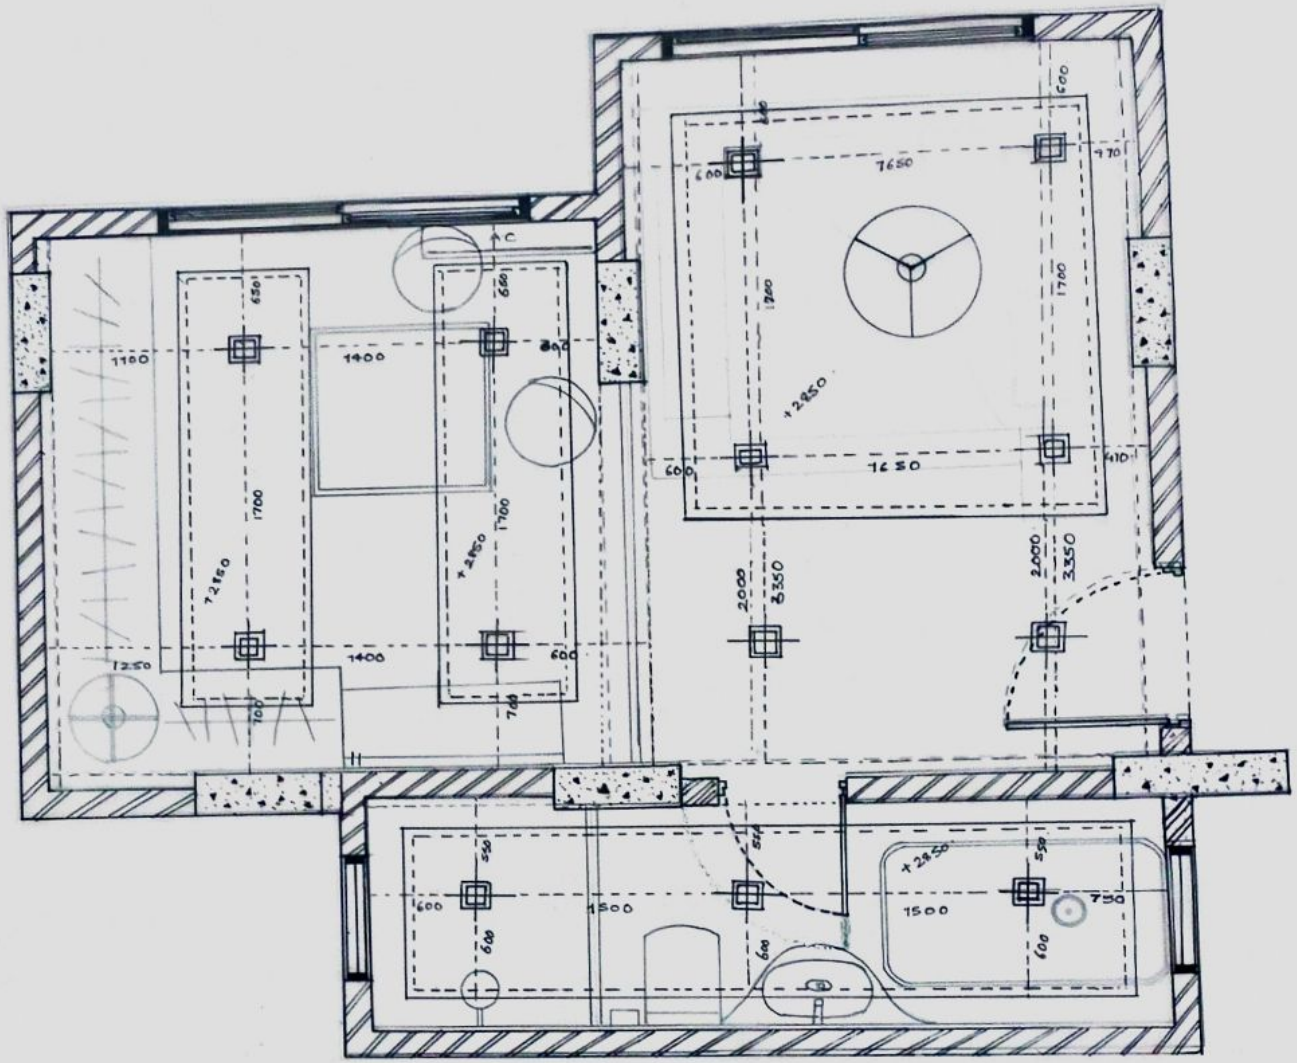

ACADEMY OF ARCHITECTURE
B.VOC (Interior Design)
MUMBAI

TOPIC
BEDROOM PLAN
CEILING PLAN

NOTE: ALL DIMENSIONS AND LEVELS ARE IN MILLIMETERS

SHEET NO:	NAME: URVI G ERAGOLA
SCALE: 1:15	YEAR AND CLASS: FYBVOC MARKS:
DATE	ROLL NO: 14

SIGNATURE AND REMARKS:

LEGENDS


SR NO	FURNITURE	LENGTH	WIDTH	HEIGHT
1	KINGBED	2000	1800	600
-	FOOTSTOOL	1500	450	500
3	SIDETABLE	450	450	450
4	RUG	2500	2000	5 MM
5	CHAIR	450	450	600
6	WARDROBES	600	-	2400
7	TABLE	1000	1000	800
8	BATHTUB	1500	800	600
9	W.C			450
10	WASHBASIN			800
11	SHOWER CUBICAL			2000
12	DRESSING TABLE			800



BRAND:- INDIA MART
MATERIAL:- WOODED
COLOR :- BROWN
SIZE :- 1200x190 mm
PRICE:- ₹550 sq ft
THICKNESS:- 20mm




BRAND:- ETSY
MATERIAL:- NERO MARQUINA MARBLE TILE
COLOUR:- BLACK
SIZE:- 600x600 mm
PRICE:- ~~₹300~~ ₹177
THICKNESS:- 9mm

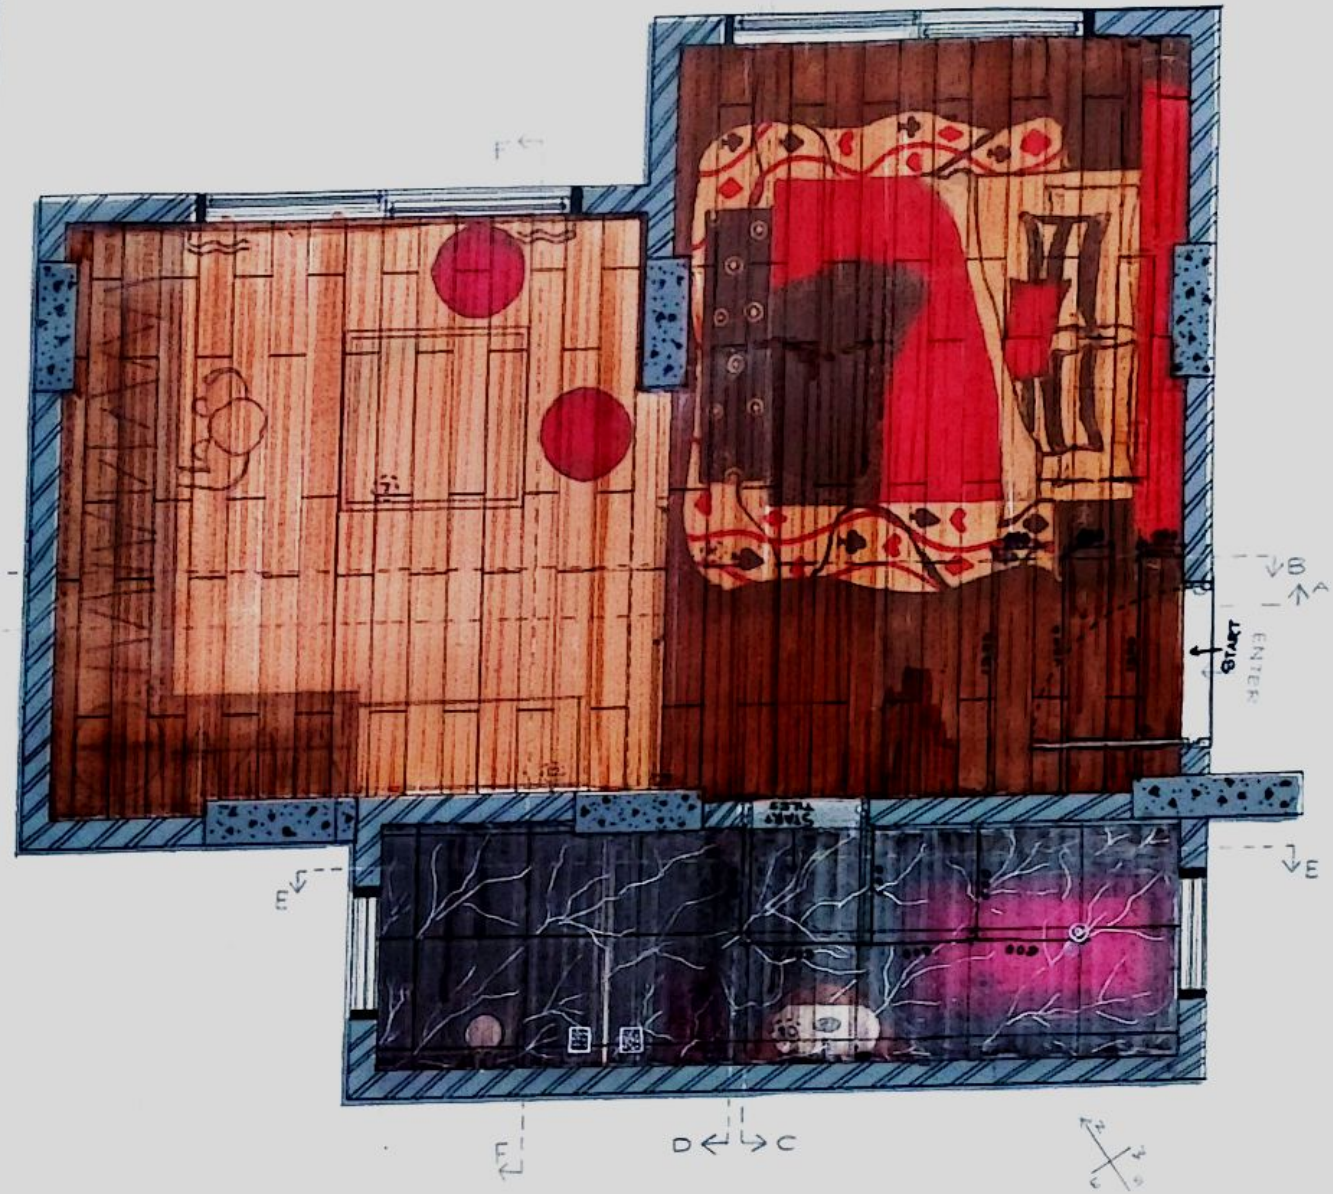

a|a MUMBAI — RACHANA SANSAD ACADEMY OF ARCHITECTURE B.VOC (Interior Design)	TOPIC: BEDROOM PLAN — FLOORING PLAN	SHEET NO: / NAME: DRVI G ERAGOLA / SCALE: 1:15 / YEAR AND CLASS: FYBVOC / MARKS: / DATE: / ROLL NO: 114 / SIGNATURE AND REMARKS

LEGENDS

SR NO	FURNITURE	LENGTH	WIDTH	HEIGHT
1	KINGBED	2000	1800	600
2	FOOTSTOOL	1500	350	500
3	SIDETABLE	450	450	450
4	RUG	2500	2000	5 MM
5	CHAIR	450	450	600
6	WARDROBES	600	-	2400
7	TABLE	1000	1000	800
8	BATHTUB	1500	800	600
9	WC	500	450	450
10	WASH BASIN	450	300	800
11	SHOWER CUBICAL	1250	1350	2000
12	DRESSING TABLE	1200	500	800

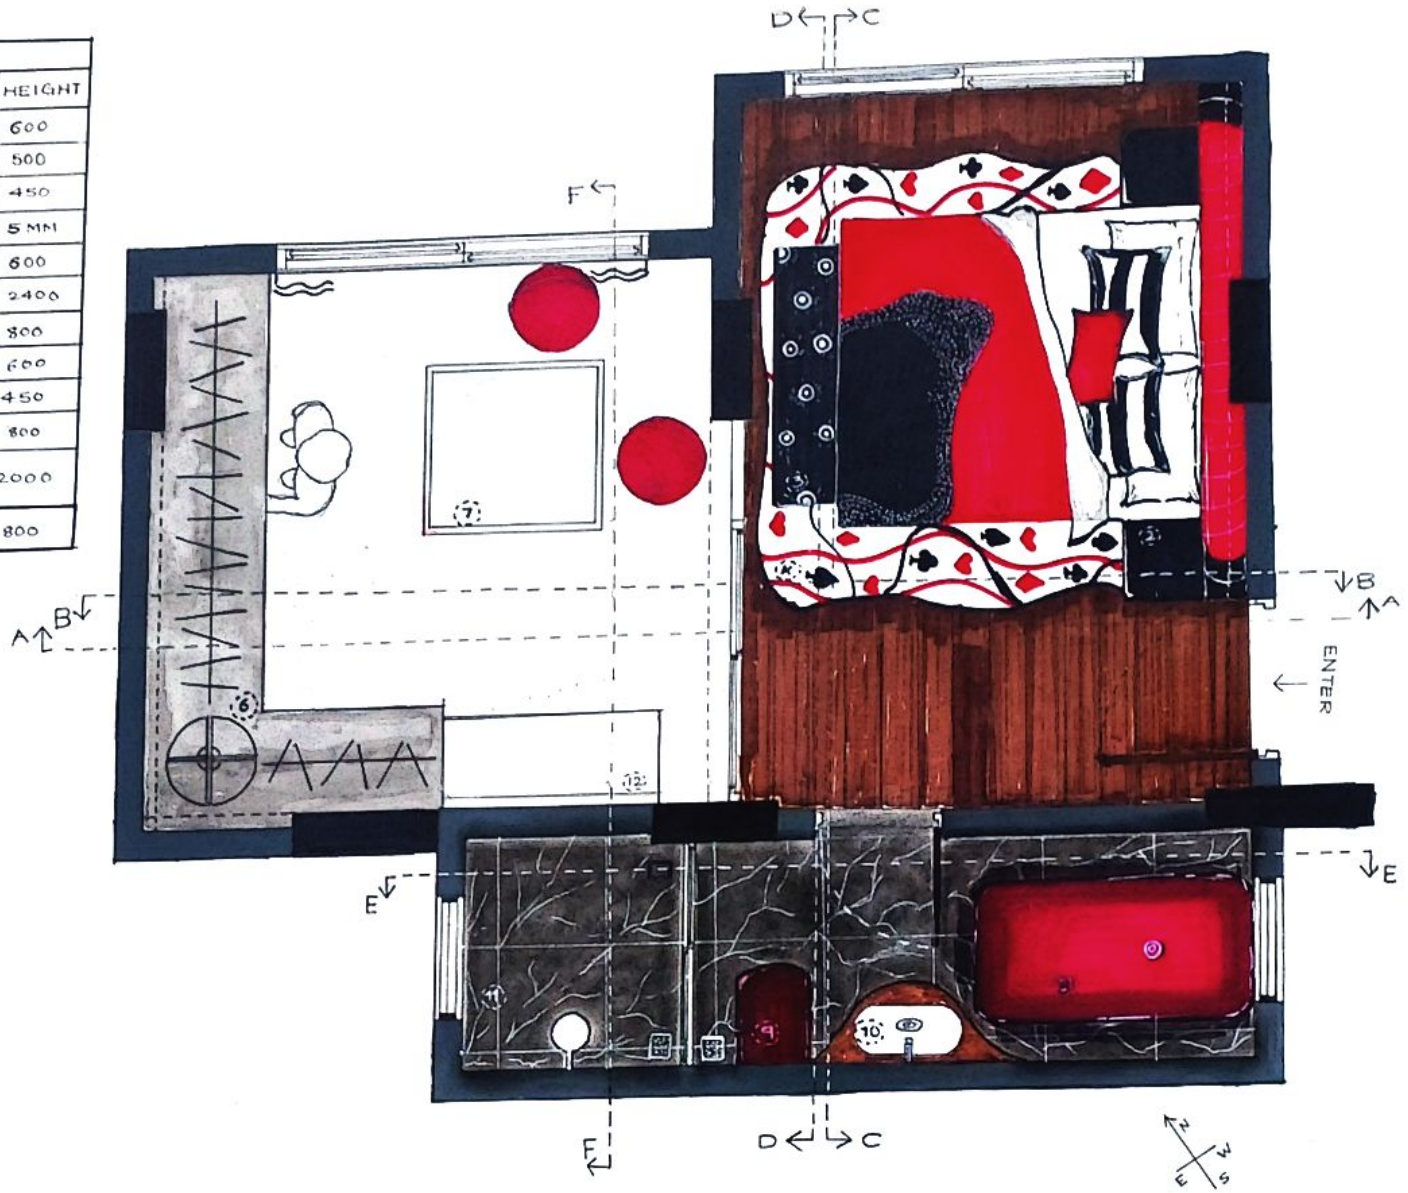

RACHANA SANSADS
ACADEMY OF ARCHITECTURE
B.VOC.(InteriorDesign)
MUMBAI

TOPIC: BEDROOM PLAN

SHEET NO:	NAME: URVI G ERAGOLA	SIGNATURE AND REMARKS
SCALE: 1:15	YEAR AND CLASS: FYBVOC	MARKS:
DATE:	ROLL NO: 14	



SECTION




SECTION 'D;D'

A0A	TOPIC: SECTION 'C,C' SECTION 'D, D"	SHEET	SCALE:	NAME: URVI G ERAGOLA
		SCALE	ROLL NO 14	SIGNATURE
		DATE	CLASS AND YEAR FYBVOC	MARKS:



SECTION 'AA'

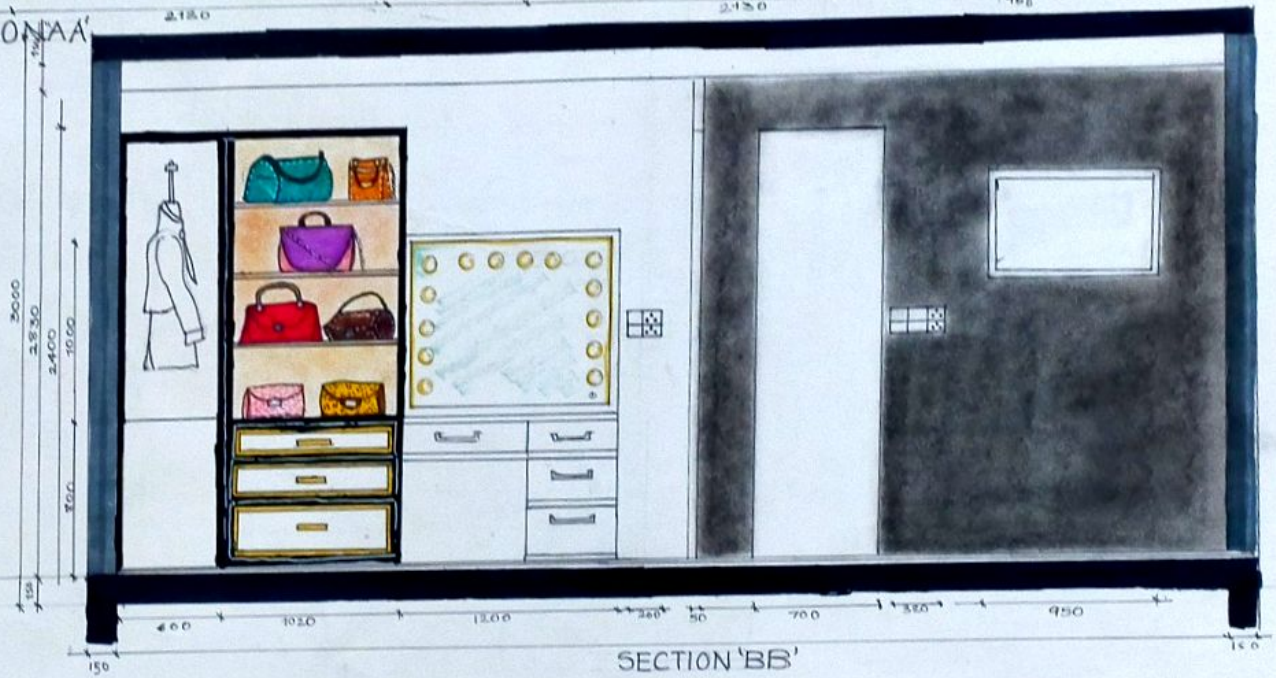

SECTION 'BB'

RACHANA SANSADS ACADEMY OF ARCHITECTURE B.VOC.(Interior Design) MUMBAI	TOPIC: SECTION 'A;A' - SECTION 'B,B'	SHEET NO.:	NAME: URVI G ERAGOLA
		SCALE:	YEAR AND CLASS: FYBVOC
		DATE:	ROLL NO.: 14
			MARKS:
			SIGNATURE AND REMARKS:



SECTION 'E;E'

A0A	TOPIC: SECTION 'E-E' & SECTION 'F-F'	SHEET	SCALE	NAME: URVI G ERAGOLA	
		SCALE	ROLLNO:	MARKS	SIGNATURE AND REMARK:
		DATE:	CLASS AND YEAR		